

DESIGN

PO
RT
FO
LIO

AR. DIVYA RASTOGI
SELECTED WORKS



Divya Rastogi, I am an architect by profession & an artist by passion.

EDUCATIONAL QUALIFICATION -

School - Carmel Convent BHEL, Bhopal 2012

Bachelor's of Architecture - 5 Years
Bharati Vidyapeeth Deemed University
College of Architecture, Pune - 2017

Maan Singh Tomar Degree in Arts One
Year at KALA ASHRAM - 2018

Certification in Advance Tattooing - 2021

Certification in all body Piercings - 2022

Certification in Advance UI UX Design
IIIT Bangalore/Simplilearn
2023 - CURRENT

SPECIALITIES -

User Centric Design abilities, Presentation Skills, Organised Work, Creative, Dedicated to designated work, Curiosity to learn, Excellent communication skills.

SOFTWARE SKILLS -



EXPERIENCE -

Assistant Prof. at IPS Academy, School of Architecture, Indore.

Along side I have many ongoing projects in MP, majorly residential and landscape.

Worked as Tattoo Artist at OZ Tattos, New Delhi, With different types of client, managed studio as a fresher artist I got alot of exposure.

Worked as an associate Architect at Archidea, Bhopal.

Worked as a Landscape Designer with Margosa Landscapes, New Delhi.

Worked as an Intern with Kushwah & Kushwah Architects, Bhopal.

EXTRACURRICULAR ACTIVITIES -

Tattooing for the love of art since 2021 - Current

Digital Freelancing Marketing - Feb 2021 to Dec 2021

Three Consecutive Biennales -
2017 - Worked as a Project head under artist Marinella Senatore.

2015 - Worked as a head volunteer in three different Projects. Wall painting, a Sculpture, An Installation.

2013 - Volunteered in the management of the event to understand the functioning of the biennale.

Wall Paintings -
ONYX Mall (Pune, India),
Competition - Stood 4th Amongst 60 Teams,
Niwara Old age Home
(Pune, Part Of Pune Biennale Management).

Stone Paper Scissor - Art & Architecture Exhibition
Organized By University. (Presentation Work on Opening Ceremony).

SKILLS



LANDSCAPE
DESIGN



PAINTING



TATTOOING



TEAM WORK



CREATIVE
THINKING



LANDSCAPE DESIGN


FARMHOUSE LANDSCAPE DESIGN

CONCEPT DEVELOPMENT

DESIGN DEVELOPMENT



In this landscape design we sought to transform this farmhouse into a haven that celebrates the serenity of the countryside while offering a touch of elegance and modern comfort. The seamless integration of natural elements and functional spaces ensures a harmonious retreat where residents and guests can connect with nature, rejuvenate their spirits, and embrace the timeless allure of rural living.

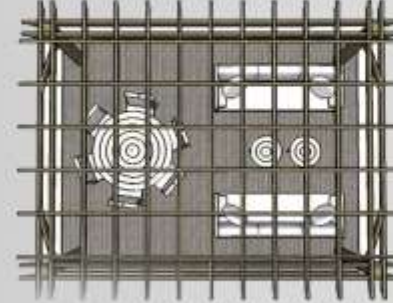


Elements used to bring life to the design.



The "Rural Elegance Retreat" landscape design for this farmhouse combines the timeless charm of the countryside with sophisticated and functional elements.

Doordarshan Delhi - ENTRANCE/BUILDING ENHANCEMENT

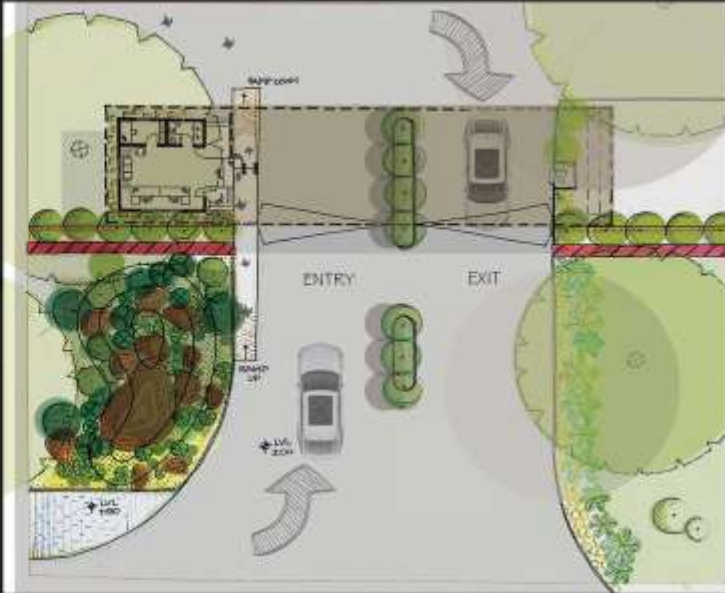

CREATION OF MOOD AND EXPERIENCE WHEN
A PERSON WALKS INTO THE SPACE

PROJECT LOCATION : NEW DELHI
PRASAS BHARTI (DOORDARSHAN)
ARCHITECT : RAJ REWAL



5. NORTH SIDE ISLAND (Seating Area With Island)-



1. MOUND



4. SEATING MATERIAL



2. SEATING



5. PLUMERIA WITH SMALL SHRUBS



3. SCULPTURE WITH PLANTS




6. SMALL POCKETS OF PLANTS

6. EXTREME NORTH -



SECTION - EE'

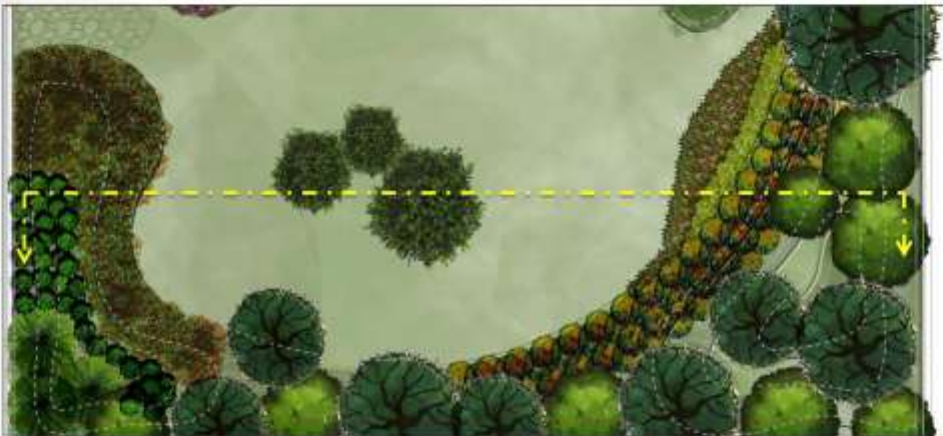

PLANTS ON MOUND




6. SOUTH SIDE - CORNER SEATING-






ARCHITECTURAL DESIGN



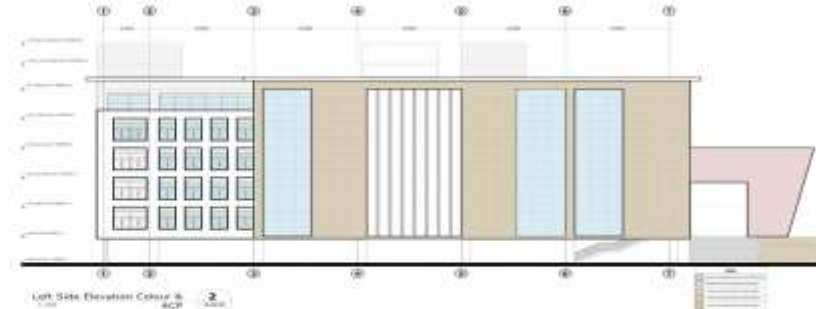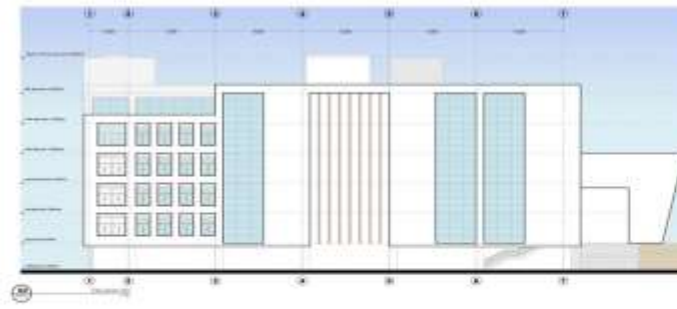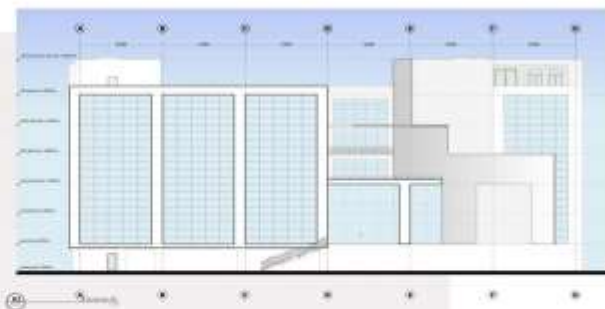

Left Side Elevation Colour & ACP

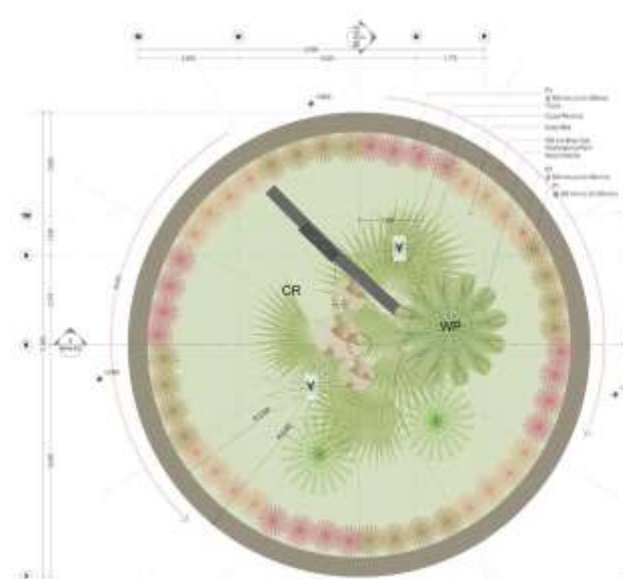

1. Detail C Plan



2. Section




3. Section



4. View (Detail C)



9. View (Detail D)

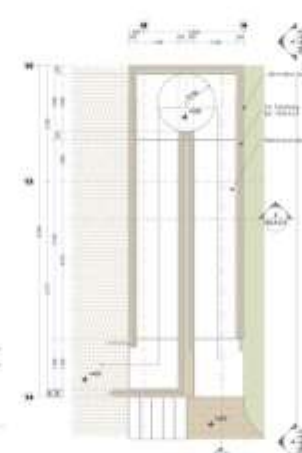

6. Detail D Plan



6. Elevation



7. Section




8. Section



10. Detail



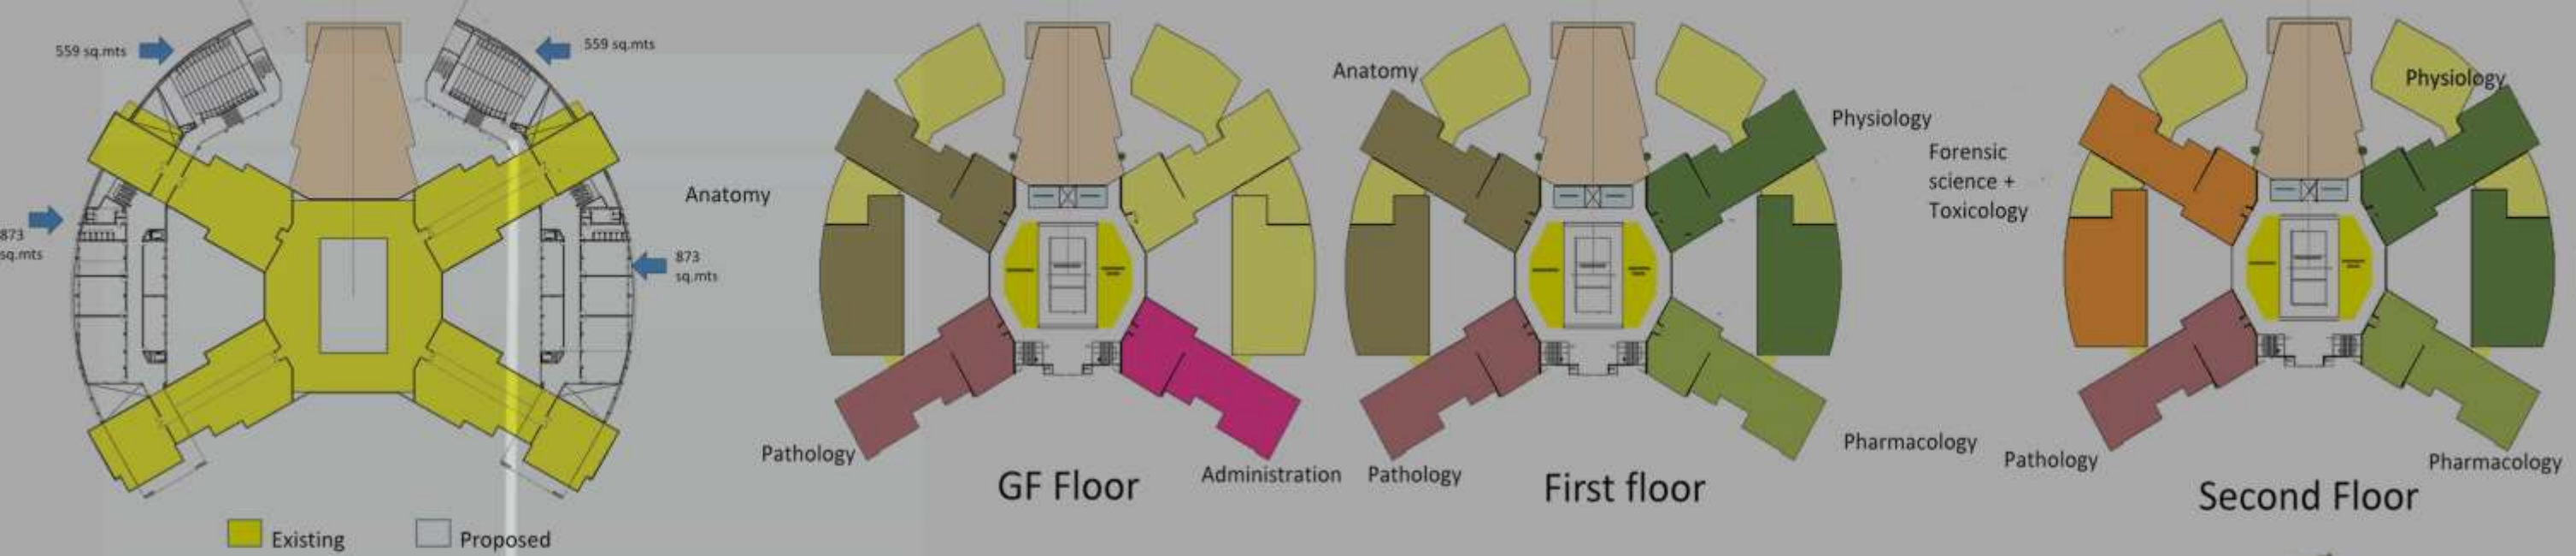

Proposed Upgradation Project of Gandhi Medical College
Hamidia Road, Bhopal, MP



EXISTING SITE



PROPOSED SITE



PROJECT LOCATION : BALAGHAT MP
MANDI/SMALL COMMERCIAL HUB






ACADEMICS

3

INTRODUCTION TO MAHESHWAR :


- o The peaceful, riverside town of Maheshwar has long held spiritual significance – it's mentioned in the Mahabharata and Ramayana under its old name, Mahishmati, and still draws sadhus and pilgrims to its ancient ghats and temples on the holy Narmada River.
- o The town enjoyed a golden age in the late 18th century under Holkar queen Ahilyabai, who built the palace in the towering fort and many other monuments.
- o Away from the ghats and historic buildings, Maheshwar's streets exhibit colorful Maheshwari Sarees

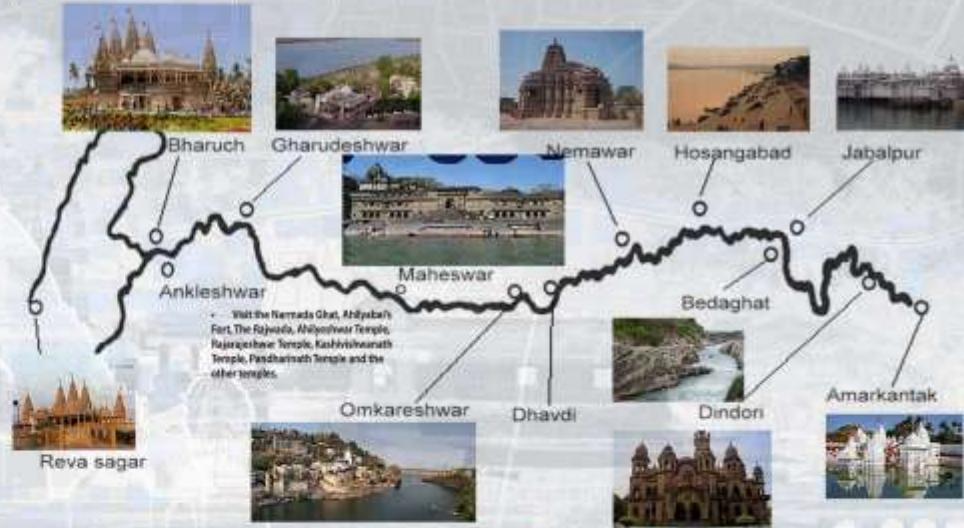


CLIMATE

Maheshwar is influenced by the local steppe climate. In Maheshwar, there is little rainfall throughout the year. The average annual temperature in Maheshwar is 27.1 °C. The average annual rainfall is 801 mm.

It falls under low rainfall area average rainfall of 980 mm.
temp. in summers - 30 c to 45c
winter- 10c to 3c
highest flood level - 5m above the ghat level
wind direction from feb to oct - S-W TO N-E
nov to jan - N-E TO S-W

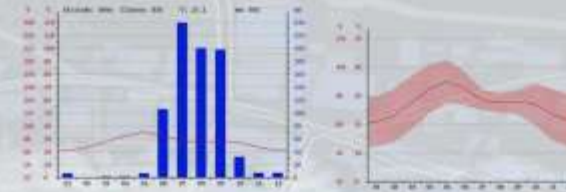

Geographical location	22.11°N , 75.35°E
Min. temperature	3°C
Max temperature	45°C
Average annual rainfall	801mm
Humidity	55%
Average wind speed	18km/h

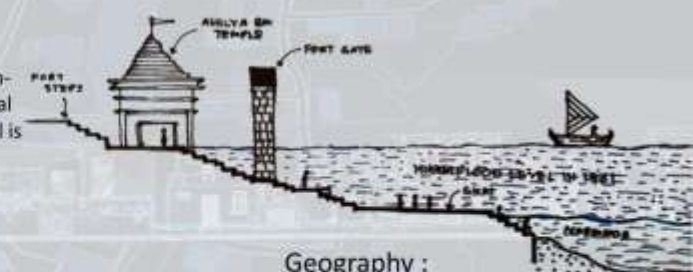

Geography :

maheshwar has vindhyachal range in south and satpura range in south. 250 m above sea level.
alluvium on basin and flood plains.



Demographic data of Maheshwar acc. to 2011 census

		Persons	Male	Female
1. Population	Total	2,32,973	1,18,340	1,14,738
	Rural	1,96,224	99,534	96,690
	Urban	36,754	18,750	18,040
2. Children (0-6 years)	Total	32,013	16,511	15,502
3. Literacy rate (%)	Total	68.8	79.8	54.1



NOV. - FEB.



MARCH - JUNE



JULY - OCT.



The floor plan shows a rectangular building with a total width of 12.0 and a total depth of 11.0. The layout includes a central square room (2.40 x 2.40) with a fireplace, a kitchen (3.20 x 3.20) with a sink and stove, a bathroom (1.40 x 1.40) with a toilet and shower, and a bedroom (1.40 x 1.40) with a bed. There are also two smaller rooms (1.40 x 1.40) and a large living area (1.40 x 1.40). The plan is labeled with various symbols and dimensions, including a north arrow and a scale bar.

Architectural floor plan of a house with dimensions and room labels. The plan includes a kitchen (2.8 x 3.16), a dining room (2.6 x 5.16), a living room (2.8 x 1.2), a water tank, and a staircase. The overall dimensions are 12.0 x 25.50. The plan also shows a section of the house with a staircase and a door, with dimensions 1.70 and 0.60. The plan is labeled 'FLOOR PLAN' and 'SCALE 1:100'.

SCALE 1:10

WOODEN ARCH (MAHIRAP)

1.15

The drawing illustrates a 'PROJECTED WINDOW' with two views: an elevation and a section.

- Elevation View:** Shows the front of the window. It features a decorative arch with a central dome and a base with ornate carvings. The total height is 2200 units. The base is divided into two sections, each 500 units wide, with a total width of 1000 units.
- Section View:** Shows the side profile of the window. It indicates a height of 400 units for the main structure and a width of 500 units for the base.

ELEVATION
SECTION
PROJECTED
WINDOW

Maheshwar is a historical town located in the Khargone district of Madhya Pradesh, India. It holds immense cultural and historical significance, and it's renowned for its rich heritage, temples, and traditional architecture. We did a detailed research on the designs and the ornamentation done.

Kumbh-mela the Hindu pilgrimage. India is such a magnificent country which is known world-wide for its unity in diversity. Being world's biggest democratic nation, India is also known for variety of festivals, some of them have global fame, too. Kumbh Mela is such a mega event with global reputation. They take a holy bath in the river which is said to bestow salvation to the devotees and absolve them off sins and sufferings. Such is the religious magnificence of Kumbh Mela that tourists from different parts of the world come to witness this grand festivity of India.



Simhasth Maha Kumbh is rejoiced by holy dip in the sacred river Kshipra in incant and religious city Ujjain (Madhya Pradesh). The Great Simhasth Kumbh maha parva is based on the celestial lineup of Planets and the Signs of the Zodiac which occurs every 12 years

SIMHASTHA The great bathing festival of Ujjain

Duration: Ceremonial bathing in the holy waters of kshipra begins with the full moon day of chitra month and continues throughout the succeeding month of th Vaishakh culminating on tenth full moon day.

Floating Population
Over all: 2 to 3 crore
Per day: 10,00,000 to 15,00,000



Most significant days during kumbh mela

1. Makar sakranti
2. Paush Purnima
3. Mauni amavasya snan
4. Basant panchami snan
5. Rath saplami snan
6. Bhisama ekadashi snan



Astrological context

When the planets have reached their maximum alignment, the gathering begins at the banks of the holy Ganges, Yumuna, and mythical Saraswati rivers: Jupiter enters Aries at this special time when the bubbling waters of the underground Saraswati River can also be seen merging with the blue waters of the Ganges and the green Yumuna River



Ujjain, Kshipra
kumbh/simhastha

Nasik, Godawari
Kumbh/Simhastha



Haridwar, Ganga
-Ardh kumbh
-Kumbh

Allahbad, Ganga
-Ardh kumbh
-Purna kumbh
-Maha kumbh



Bathing Activity	Day from Hindu Calender	Day
Pratham Shahi Snan	Chaitra Sukla Purnima	1
Mesh sakarant		8
Panchkroshi Yatra	Vaishak Krishna Dashmi	10-15
Parva Snan	Vaishak Kraishna Amavasya	15
Dwitya Shahi Snan	Akshaya Tritiya	18
Parva Snan	Shankaracharya Jayanti	20
Antim Shahi Snan	Vaishak Sukla Purnima	30

SIGNIFICANCES OF UJJAIN FOR SIMHASTHA

Puranas: legendary churning of the oceans by the Gods and the Demons yielded amongst a jar of nectar.

The gods did not like to share it with the demons. At the instance of Indra, his son Jayanta tried to run away with the jar of nectar followed by the demons. During the struggle for its possession, lasting over twelve days in heaven, a few drops of the nectar dropped in the four places corresponding to Haridwar, Ujjain, Prayag, and Trimbakeswar on earth in the holy waters of the rivers. The struggle for the possession lasted for over twelve days in heaven equivalent to twelve years on earth.



SECTS AND AKHADAS

SECTS	AKHADAS	
SHAIVA AKHADA	JUNA	AGANI
		AHAVAN
	MAHANIRVANI	ATAL
	NIRANJANI	ANAND
VAISHNAV AKHADAS	DIGAMBAR	
	NIRVANI	
	NIRMOHI	
UDASEEN AKHADA	BADA UDASEEN	
	NAYA UDASEEN	
NIRMAL AKHADA	NIRMAL AKHADA	

Pashwai Routes

During simhastha akhadas of sadhus and saints arrive 20 to 30 days prior to kumbh mela in ujjain

Before settling at their mela grounds they settle at different grounds within the city They move from one mela ground to another with in the city in the form of procession

The procession is known as pashwai the grandiour of these pashwai can be clearly seen from their procections

It has elephants,Raths,Horses,Music bands and decorated vehicles along with the saints

Usually the main sadhu sits on the vehicle or elephant and the other smaller sects of sadhus follow them, till the akhadas



- UDASIN AKHADA
- NIRMAL AKHADA
- SHRI DIGAMBAR AKHADA
- VAISHNAV AKHADA
- SHAIVE AKHADA
- UDASIN NAYA AKHADA



Ram Ghat : During Kumbh Mela Snan

S. NO	QUESTIONS	Options	A	B	C	TOTAL
1	How long would you stay?		1 day	2-3 days	More than 3 days	
		No. of people	43	34	03	80
		Percentage	54%	42%	4%	100%

54% OF PEOPLE PREFER STAYING FOR ONE DAY

2	Whom you are travelling with?	Options	A	B	C	D	
			Alone	With Family	With Friends	With Group	
		No. of people	2	59	7	12	80
		Percentage	2%	74%	9%	15%	100%

15% TRAVEL IN GROUPS

3	What is the frequency of visit to this place?	Options	A	B	C	
			1 st Time	Frequently	Mostly	
		No. of people	19	42	29	80
		Percentage	21%	47%	32%	100%

47% FREQUENTLY VISIT UJJAIN

4	Where do you stay?	Options	A	B	C	D	
			Hotel	Guest House	Dharam shala	Relatives	
		No. of people	15	42	19	4	80
		Percentage	19%	52%	24%	5%	100%

52% PREFER STAYING IN THE GUEST HOUSE


5	Will you recommend others to visit Ujjain again?	Options	A	B	C	D	
			Somewhat Unlikely	Uncertain	Somewhat likely	Extremely likely	
		No. of people	0	3	54	23	80
		Percentage	0%	4%	67%	29%	100%

67% SOME WHAT LIKELY TO RECOMEND OTHERS TO VISIT UJJAIN

Stay Duration



Travelling With

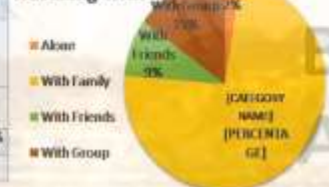

Frequency of visit



Place of Stay



Suggesting others to visit Ujjain





ART
& INKS



PERSONAL/PROFESSIONAL ARTWORKS -

Kindly note : This is my original artwork, this PDF might contain a bit of female nudity. If you find such images disturbing, Kindly skip.
Some of the artworks are sold. The artworks are not to scale Kindly refer dimensions.



POWER IN ME

Size - 11.7'' x 16.5''



Media - Digital Artwork Size
Printable upto size A3



Media - Watercolour on Paper
Size - 11.7'' x 16.5''

PERSONAL/PROFESSIONAL ARTWORKS -



Media - Acrylic on Canvas,
Size - 48'' x 34''




Media - Pen on paper,
Size - 8.5'' x 14''



Media - Paper mache
on Canvas,
Size - 48'' x 34''

PERSONAL/PROFESSIONAL ARTWORKS -

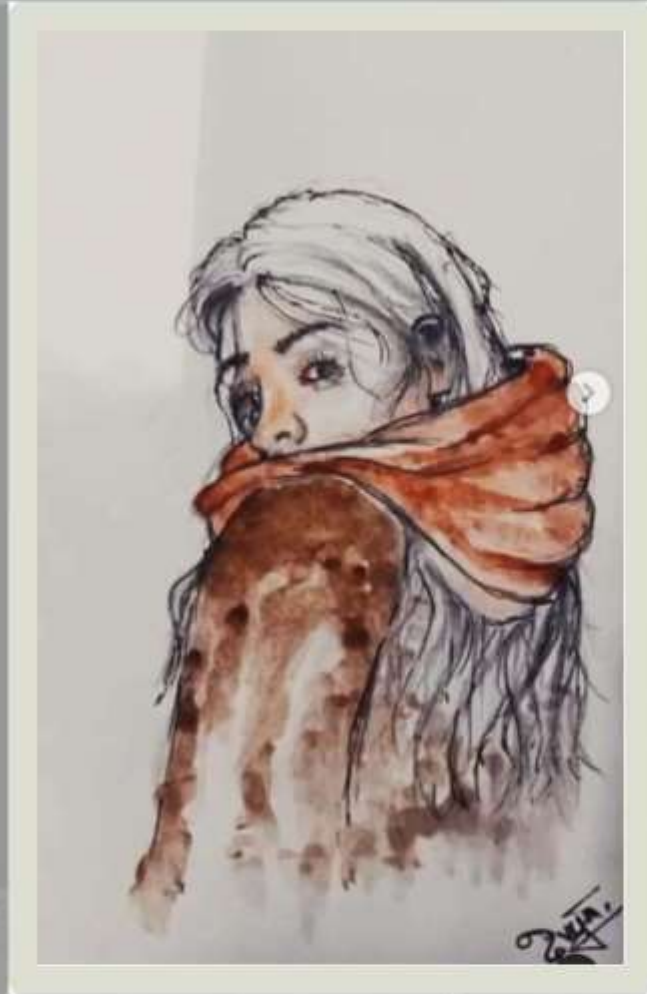

Media - Watercolour on paper

Size - 8.5" x 14"



Media - Watercolour on Paper

Size - 11.7" x 16.5"



Media - Watercolour on Paper

Size - 11.7" x 16.5"

TATTOOS -





THANK YOU
+918178560949